
Thoroughbred · Ascot home straight: site plan for sketching

Drawn to scale, north up, metres from the winning post (on the inside rail). White shapes are the site components placed today, marked with their letter (see the components sheet).
To plan: write a component's letter where you want it (an arrow for which way it faces), cross out any to remove, and give any new kind of piece a new letter (X, Y, Z…) with a quick note or sketch.

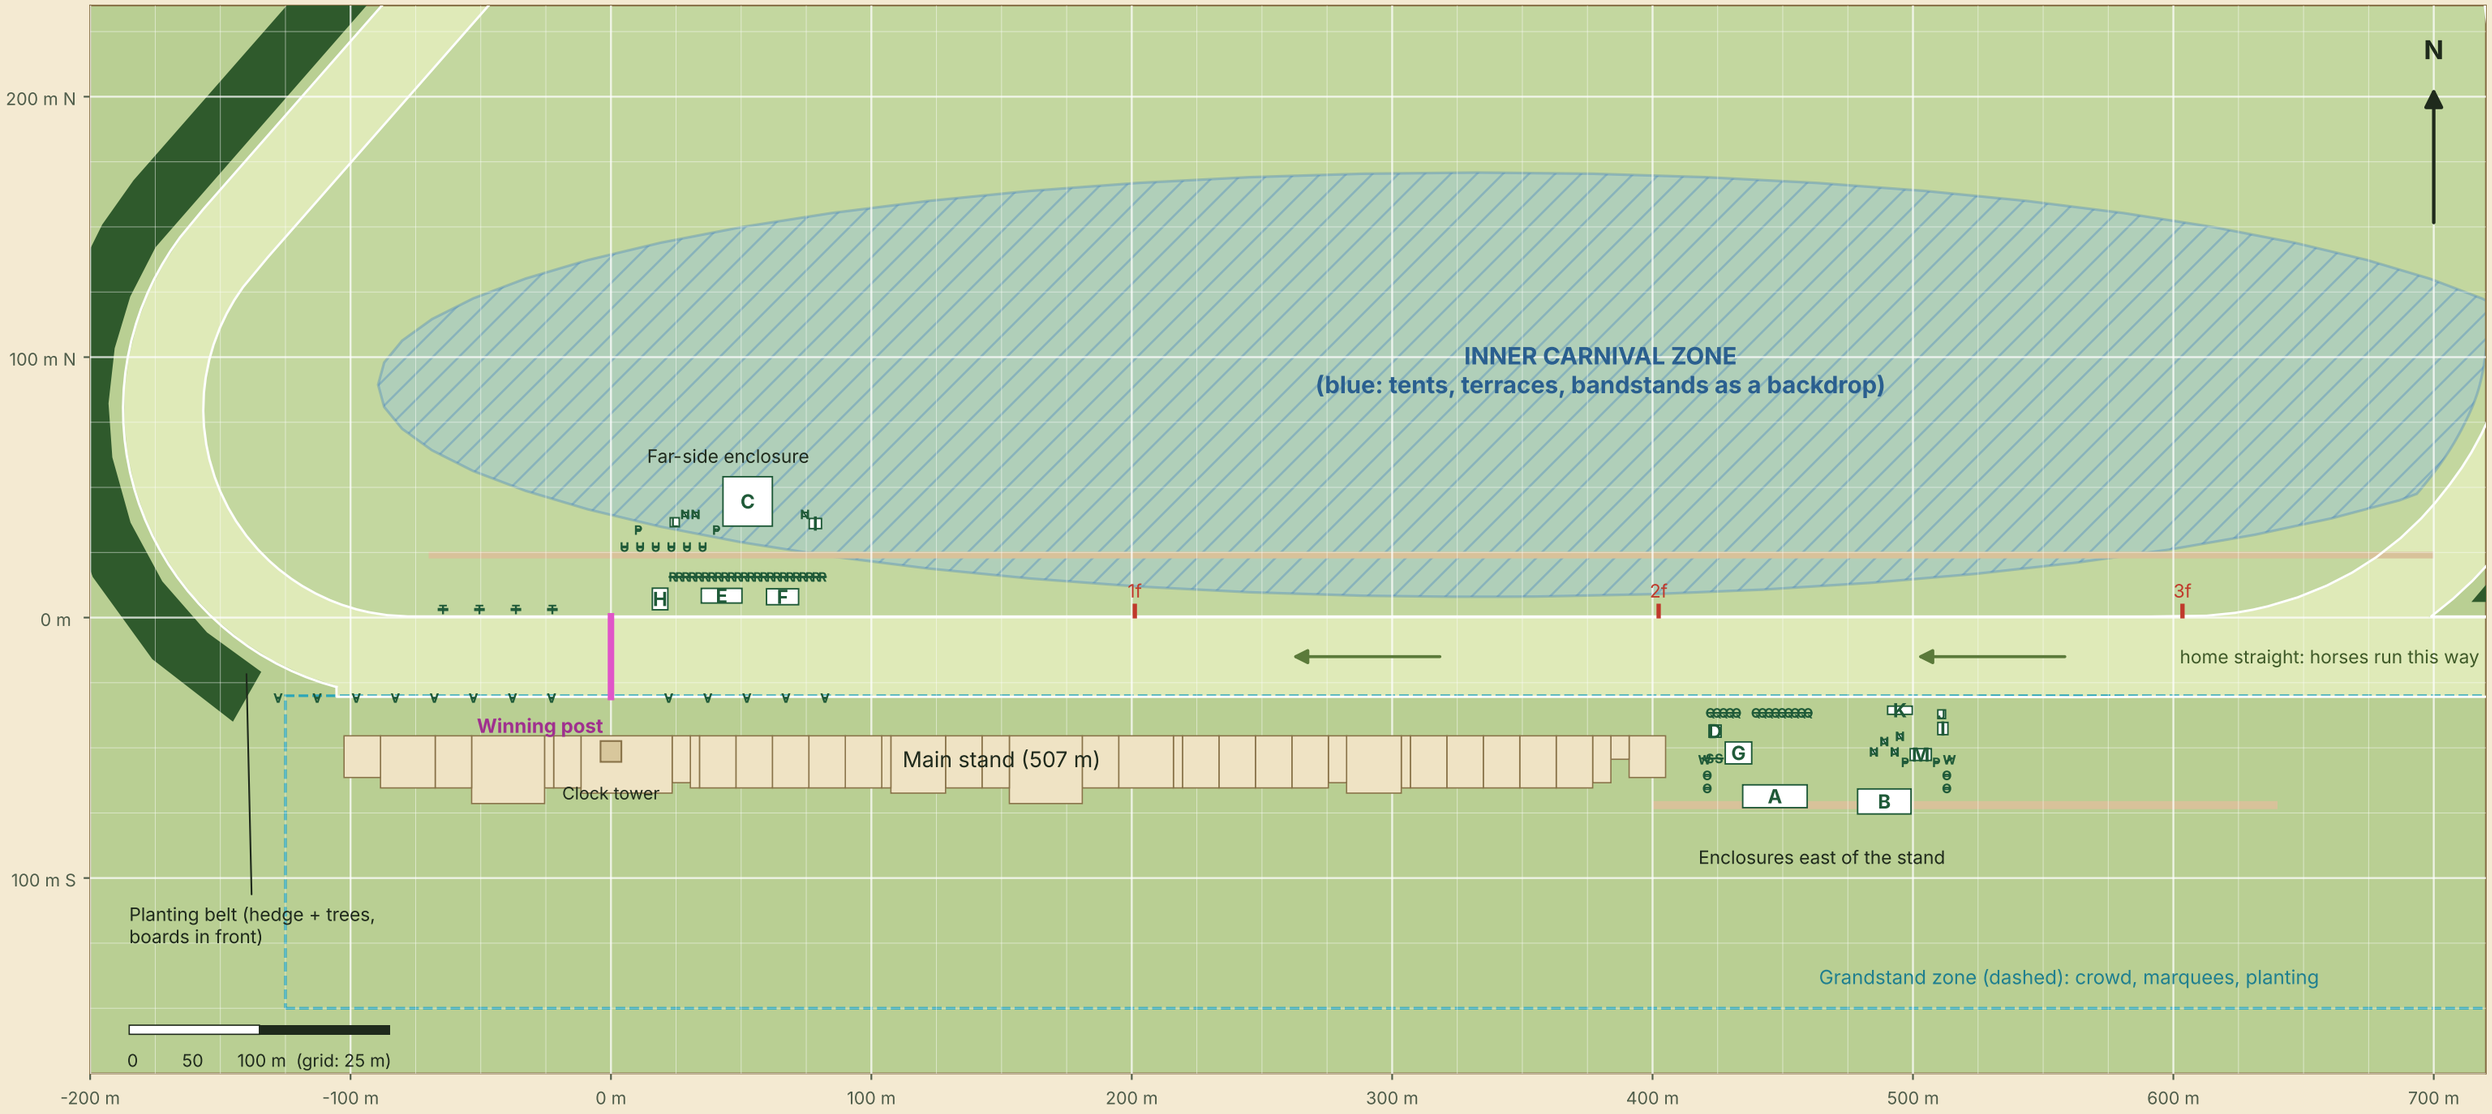

Codes

- A Three-peak marquee (24.8 × 8.8 m)
- B Glazed clearspan marquee (20.5 × 9.6 m)
- C Big top (19 × 19 m)
- D Pagoda counter (4.7 × 4.7 m)
- E Open seating stand (15.6 × 5.6 m)
- F Covered seating stand (12.3 × 6.1 m)
- G Terrace deck, parasols (10.2 × 8.4 m)
- H Viewing tower (5.9 × 8.3 m)
- I Kiosk with awning (4.7 × 3.9 m)
- J Booth hut (3.3 × 3 m)
- K Arched kiosk row (9.4 × 3.1 m)
- L Pagoda kiosk (3.5 × 3.5 m)
- M Pergola, picnic tables (8.1 × 4.5 m)
- N Picnic table (1.8 × 1.6 m)
- O Long planter (1.9 × 0.7 m)
- P Short planter (1.1 × 0.7 m)
- Q Picket fence (2.5 m) (2.6 × 0.1 m)
- R Cross-rail fence (2.5 m) (2.7 × 0.2 m)
- S Barrier rail (3.1 × 0.1 m)
- T Signboard (3.5 × 0.6 m)
- U Flagpole (1.9 × 0.5 m)
- V Banner flag (1.1 × 0.4 m)
- W Signpost (2.4 × 0.2 m)